


## Anførsler:

- Vinduer og skyvedører leveres med lakkert aluminium utside og ubehandlet laminert treverk på innside. Med unntak av V05.
- Detaljer og produksjonstegninger må fremlegges for og godkjennes av arkitekt før produksjon startes.

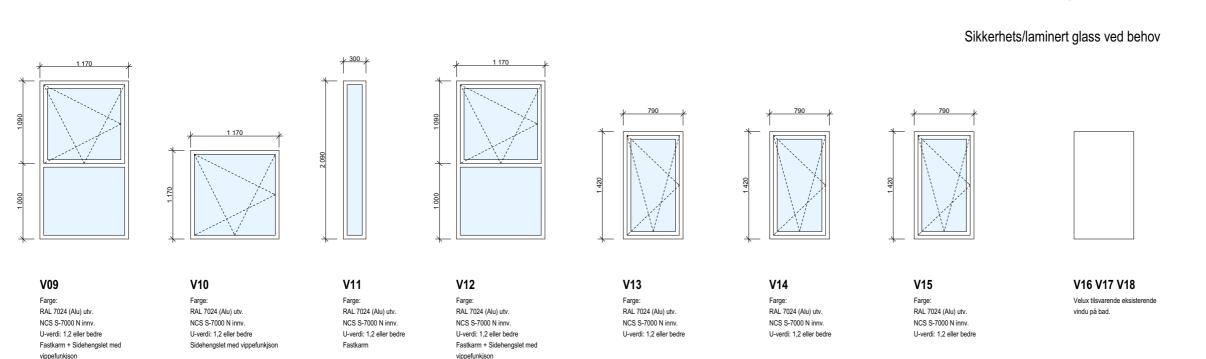

1 23.08.2016 Anbudstegninger opprettet 0 23.05.2016 Søknadstegninger opprettet

## KVALBEIN**ARKITEKTUR**

v/ Philip Kvalbein Hauge Org.Nr: 998 007 208 MVA Fabrikkgaten 5 5059 Bergen Tel: 41 20 34 44

Prosjekt:

Tilbygg To-mannsbolig Herman Grans Vei 23 C Bergen Kommune Gnr./Bnr. 153/527

Anbudstegning

Tegning: **Skjema Vinduer**Tegningsnummer: **0700**Målestokk: **1:50 / A3**Tegnet av: **PKH** 

Kontroll: **PKH** Revisjon: **1**